


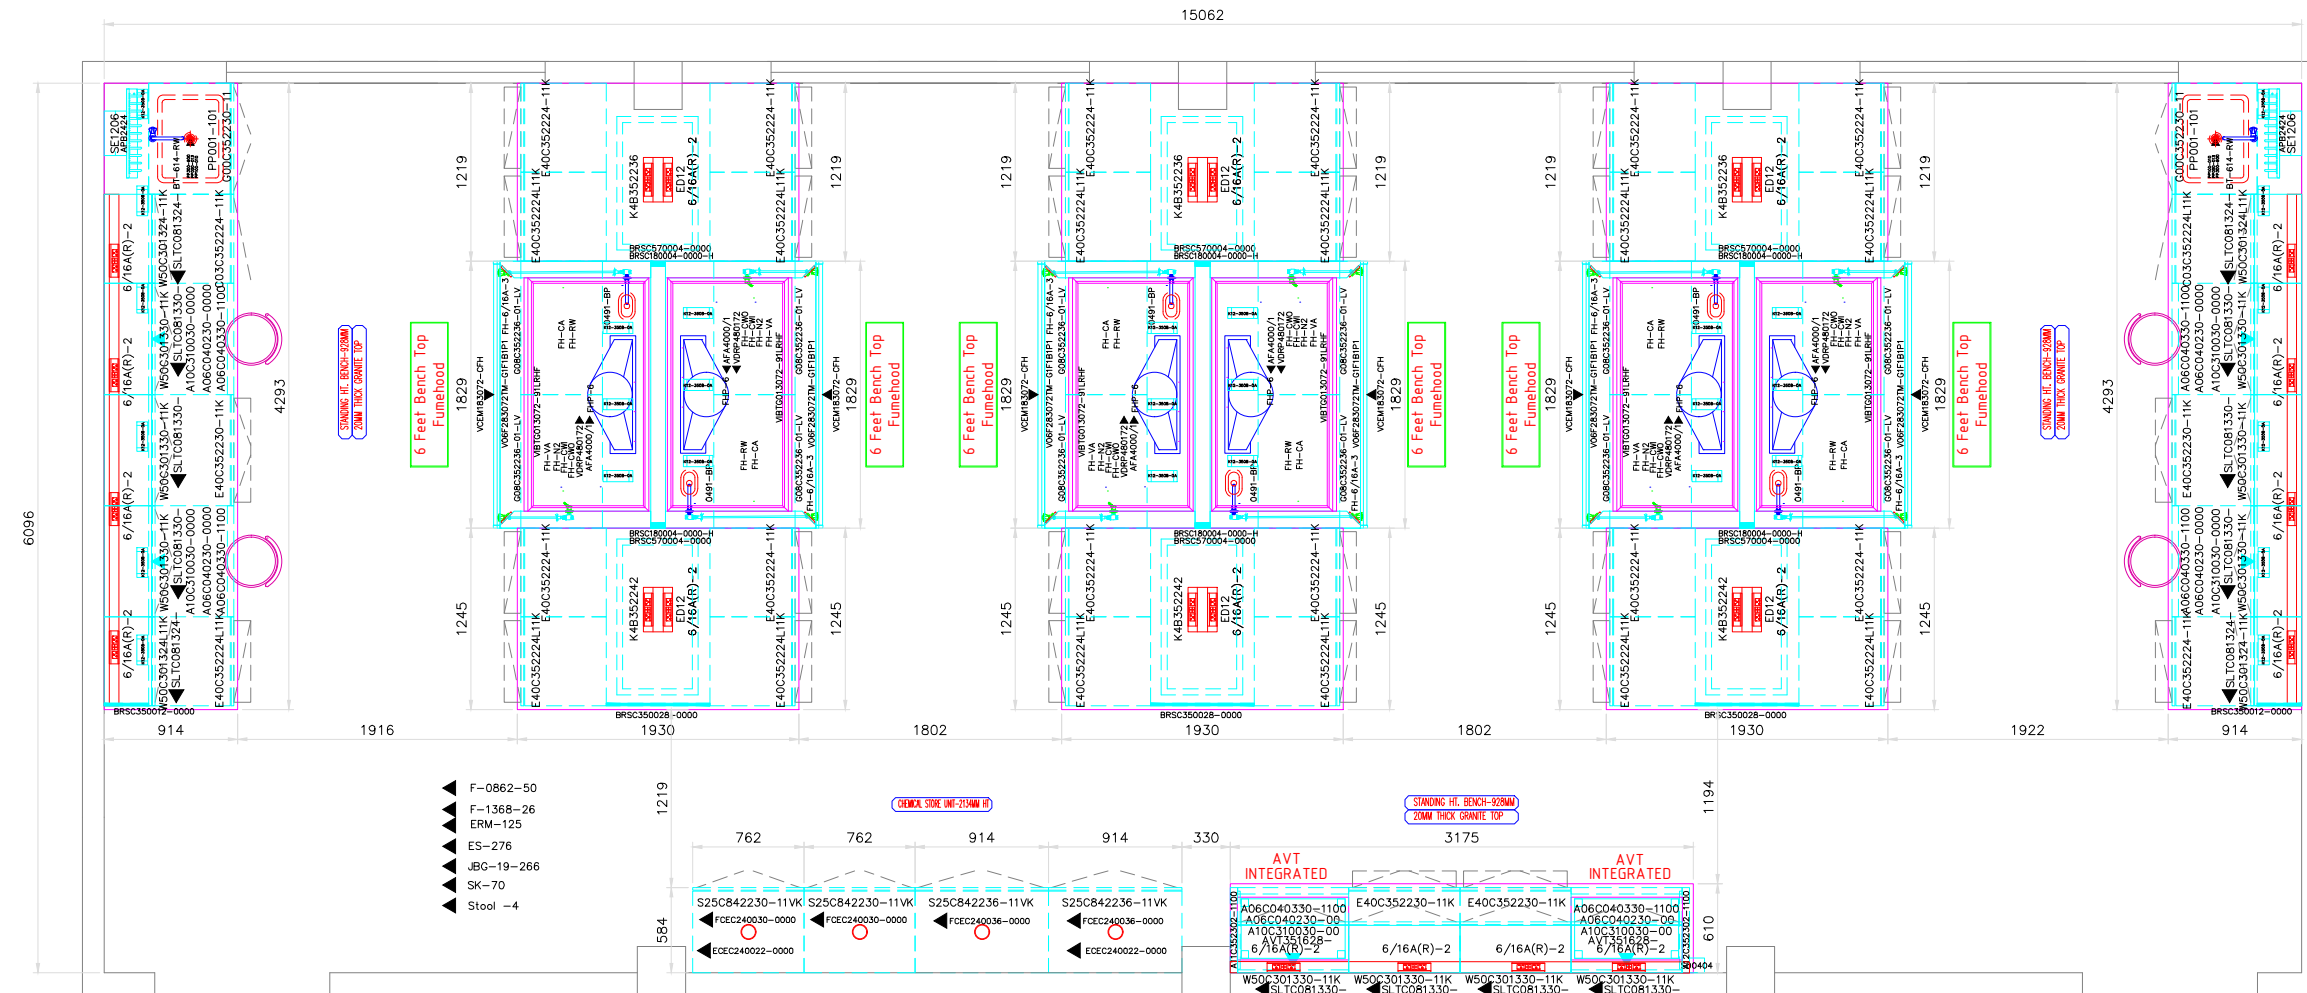


G C L FIRST FLOOR LAB PLAN LAB 1

KEY PLAN:


Building
Orientation:




Elevation Indicator

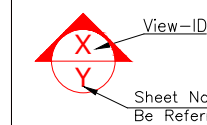


Lab Stools and Chairs
Shown are for Knee Space
Indication Purpose Only

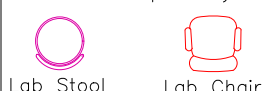

Casework Details:

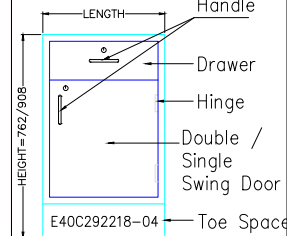

Casework Legend:

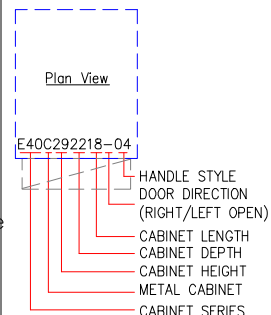

Notes:

Owner:

M/s. Spectevo Technologies Pvt. Ltd.
Hyderabad

Consultant / Architect:

Turnkey Laboratory Solution Provider:

KEWAUNEE
LABWAY INDIA PVT. LTD.

Web: www.kewaunee.in

Project Title:

PUR/2557/2020-21

Project No:

25170

Drawing Title:

Proposed Lab Furniture Layout
G C L LAB 1 First Floor
Plan View

Drawing Number:

SPE-KEW-25170-F-21

Sheet Size:

A3

Scale:

1.65

Sheet No.:

1 OF 2

Revision:

0

15062

▲ F-0862-50
▲ F-1368-26
▲ ERM-125
▲ ES-276
▲ JBG-19-266
▲ SK-70
▲ Stool -4

CHURCH SIDE (W-215MM H)

STANDING HT. BENCH-925MM
20MM THICK GRANITE TOP

AVT
INTEGRATED

AVT
INTEGRATED

BUILDING INFORMATION

TRUE CEILING	FALSE CEILING	BOTTOM OF BEAM	TERRACE ABOVE
4500	3000	NA	NA

DRAWN	CHECKED	DEPARTMENT	ISSUE DATE
Vikas	Ramya H S	LAB PLANNING	17.02.2021

FOR PROPOSAL

Drawn By:

Checked By:

Client Approval-01:

Client Approval-02:

Note:
• These Designs, Plans and Specifications therein are the property of KEWAUNEE LABWAY INDIA PVT. LTD. and must not be used, reproduced or copied wholly or in part without the written permission of KEWAUNEE LABWAY INDIA PVT. LTD., Bangalore
• All Dimension are in mm
• Kewaunee Labway India shall not be held responsible for any variation in Laboratory Furniture due to Architectural changes that have not been informed to us before hand.

REV.	Initial Proposal	VGC	09.02.2021
No.	REVISION DESCRIPTION	BY	DATE